


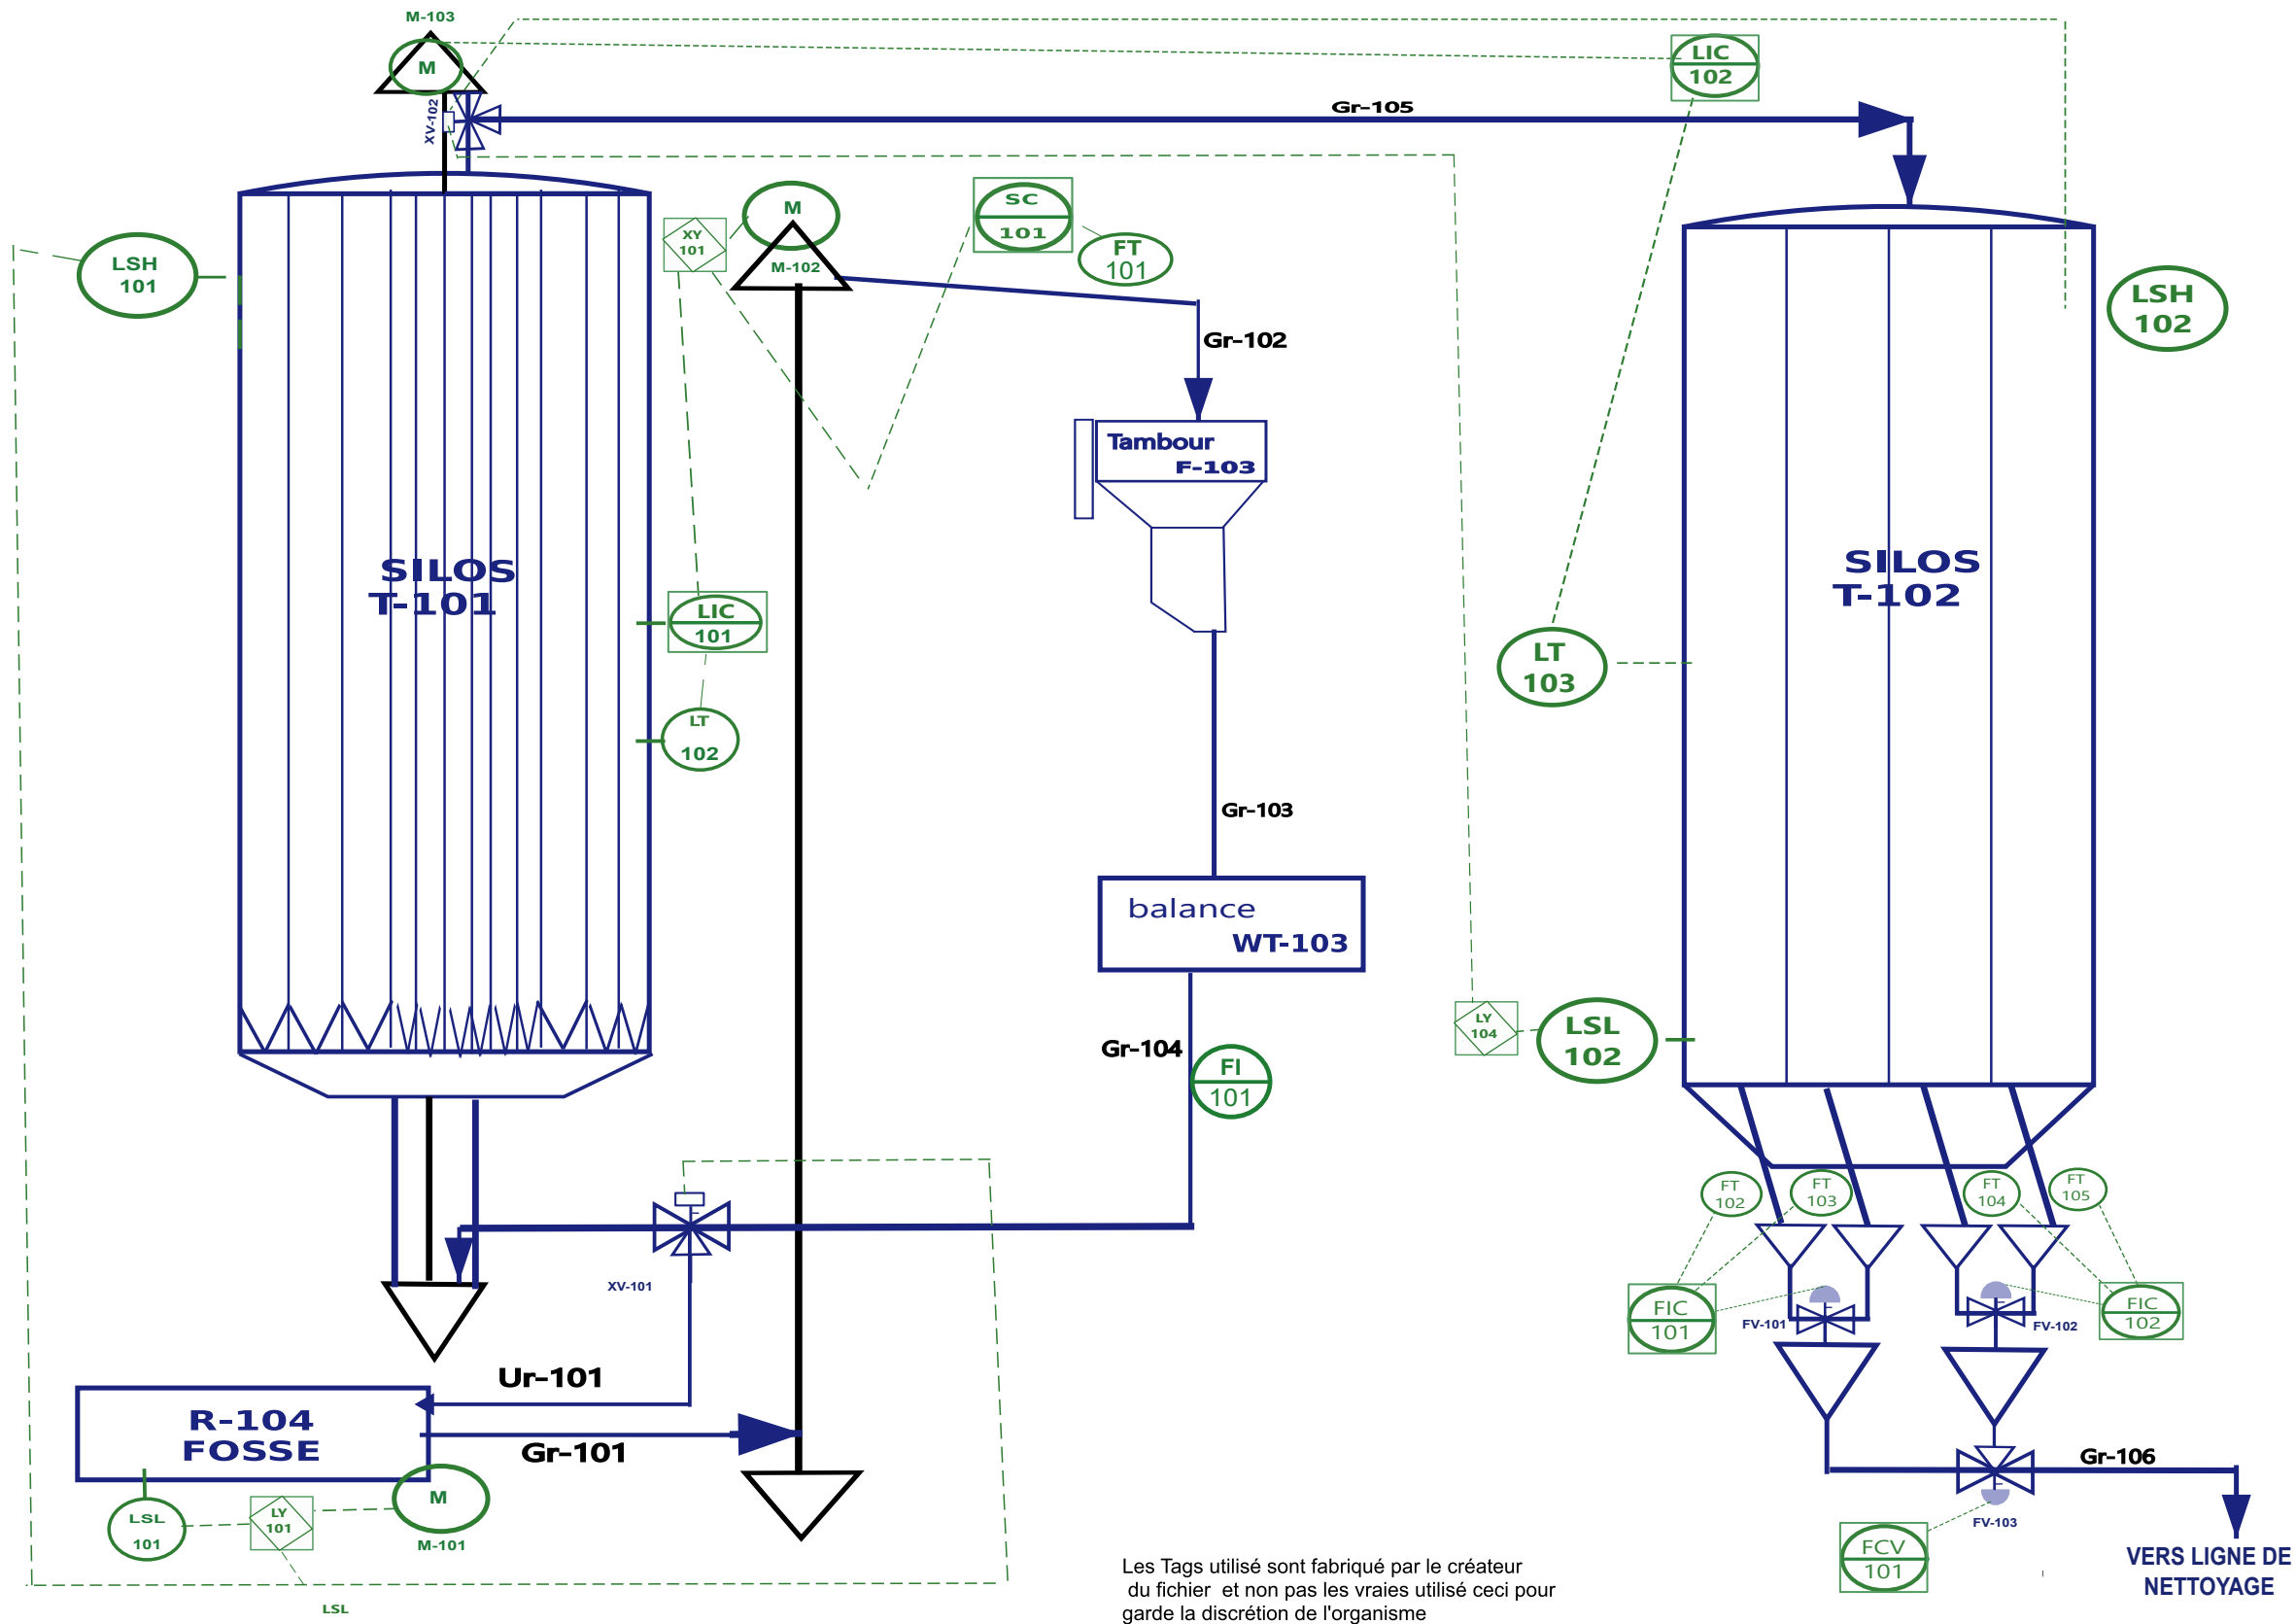

Les Tags utilisé sont fabriqué par le créateur du fichier et non pas les vraies utilisé ceci pour garde la discrétion de l'organisme

LÉGENDE

SYMBOLES

Élévateur à godets

Machine

Silo

Vanne de régulation (FV)

Vanne tout-ou-rien (XV)

Instrument (bulle ISA-5.1)

Moteur (M)

Flux procédé (grain)

Liaison de signal

CODES INSTRUMENTS (Inspiré ISA-5.1)

M

: Moteur

FT

: Transmetteur de débit

FIC

: Contrôleur indicateur de débit

FV

: Vanne de régulation de débit

XV

: Vanne tout-ou-rien

LT

: Transmetteur de niveau

LC

: Contrôleur indicateur de niveau

LSH

: Contact de niveau haut

LSL

: Contact de niveau bas

FI

: Indicateur / écran de flux

WT

: Balance de pesée

LY

: relais/calculateur de niveau

CODES ÉQUIPEMENTS

T

: Silo / réservoir

F

: Tambour de pré-nettoyage

R

: Fosse de réception

WT

: Balance

M

: Élévateur

SERVICES DES LIGNES

GR

: Grain

UR

: Grain

LIGNE	DE	VERS	PRODUIT	TRANSPORT	SECTION	INSTRUMENTS
Gr-101	FOSSE R-104	Élévateur M-102	Grain brut	Convoyeur à chaîne	Réception & Pré-nettoyage	—
Gr-102	Élévateur M-102	Tambour F-103	Grain brut	Élévateur à godets	Réception & Pré-nettoyage	FT-102, SC-101, M-102
Gr-103	Tambour F-103	Balance WT-103	Grain brut	Gravité	Réception & Pré-nettoyage	—
Gr-104	Balance WT-103	Élévateur M-101 /SILO T-101	Grain brut	Convoyeur à chaîne	Réception & Pré-nettoyage	FIG-101
Gr-105	Élévateur M-101/SILO T-101	SILO T-102	Grain brut	Élévateur à godets	Réception & Pré-nettoyage	LT-102 (signal), XV-105,LSH-102
Gr-106	SILO T-102	Ligne de nettoyage	Grain brut	Convoyeur à chaîne	Réception & Pré-nettoyage	FC-102/103, FV-102/103/104,FT-103-6

NOTES	1. Repérage des instruments inspiré selon ISA-5.1.	4. Extraction silo T-102 : boucles FT → FC → FV.
	2. Liaisons de signal en pointillés verts.	5.LC-102 en régulation continue via LT-102, et LSH-102 en tout-ou-rien (LSH en secours ultime
	3. Tuyauteries procédé : INOX.	6.UR-101 conduite de Grain qui retourne a la fosse en cas de remplissage totale des silos et peur de colmatage des conduites

PSEUDO-P&ID		
SCHÉMA LIGNE DE RÉCEPTION ET PRÉ-NETTOYAGE		
PROJET	N° DE PLAN	FORMAT
DESSINATEUR		DATE
VERSION	ÉCHELLE	FEUILLE 1 / 4