


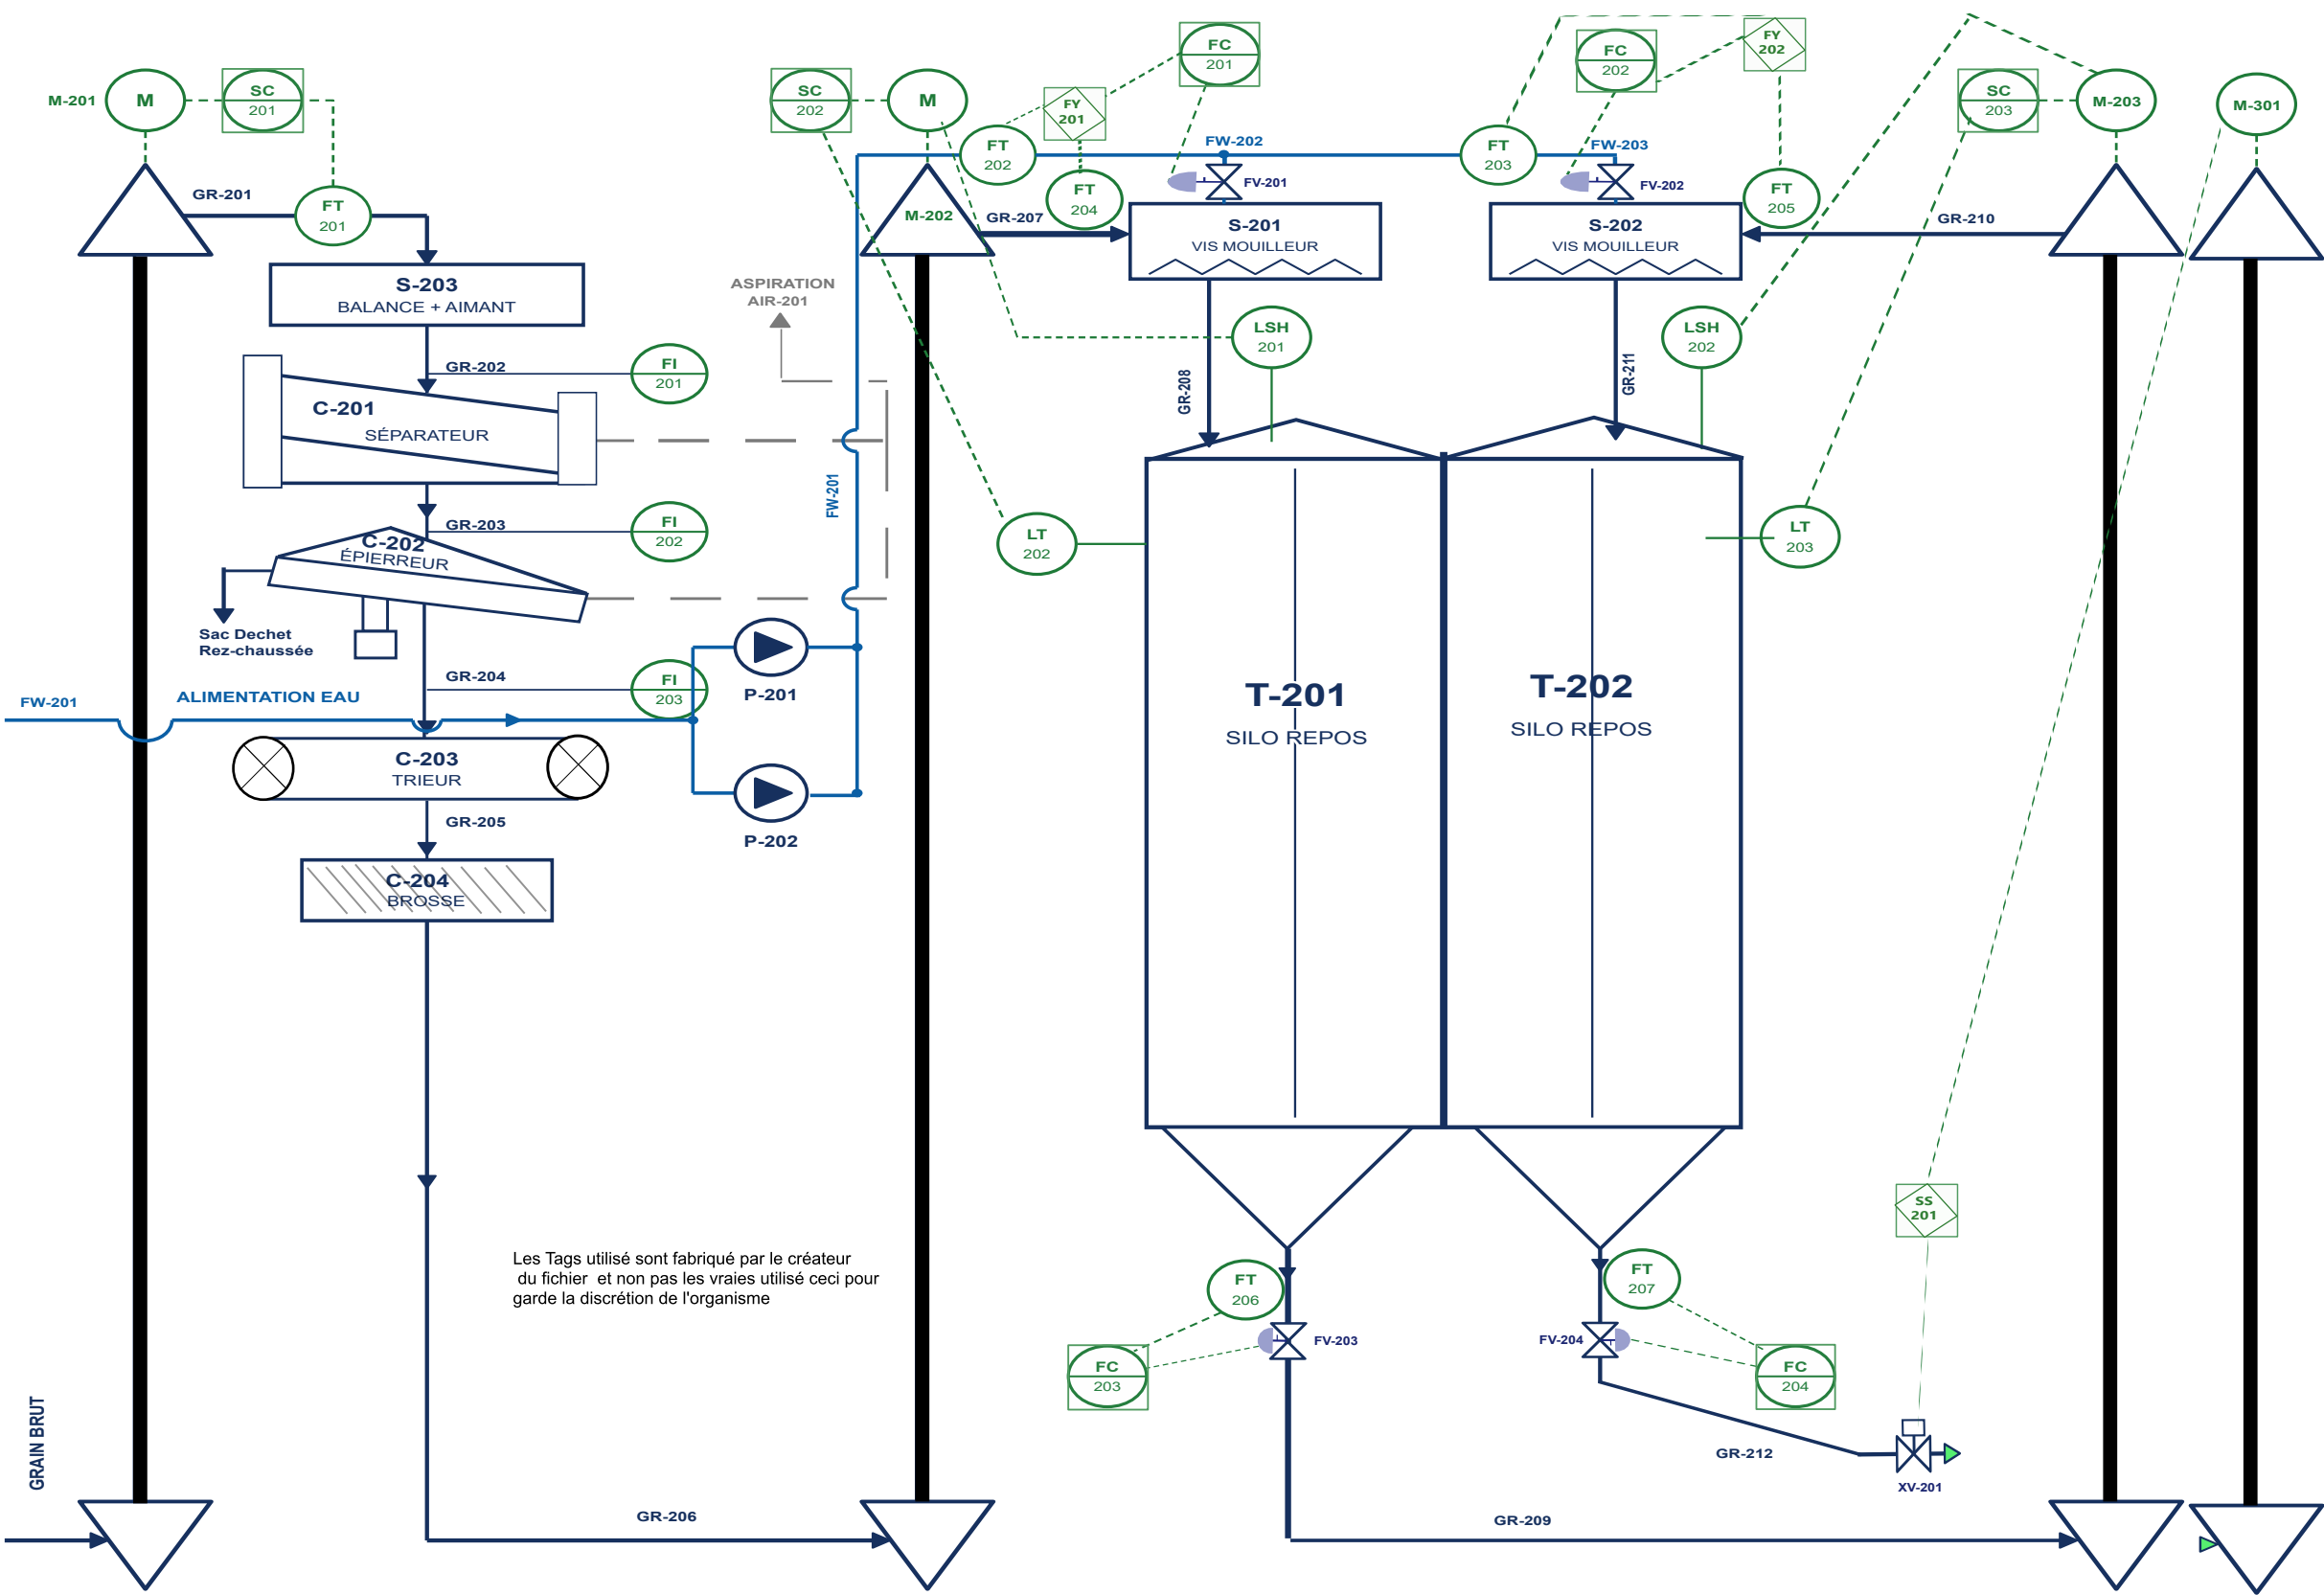

Les Tags utilisé sont fabriqué par le créateur du fichier et non pas les vraies utilisé ceci pour garde la discrétion de l'organisme

LÉGENDE

SYMBOLES

Élévateur à godets

Machine

Vis mouilleur

Silo

Pompe

Vanne de régulation

Instrument (bulle ISA-5.1)

Moteur (M)

Flux procédé (grain)

Flux eau (mouillage)

Flux air (aspiration)

Liaison de signal

CODES INSTRUMENTS (Inspiré ISA-5.1)

FC

: Contrôleur de débit

FT

: Transmetteur de débit

FV

: Vanne de régulation de débit

FI

: Indicateur / écran

LT

: Transmetteur de niveau

LSH

: Contact de niveau haut

PDT

: Transmetteur de pression diff.

SC

: Contrôleur de vitesse

M

: Moteur

CODES ÉQUIPEMENTS

T

: Silo / réservoir

S

: Vis, mouilleur

C

: Machine de traitement

P

: Pompe

M

: Élévateur

SERVICES DES LIGNES

GR

: Grain

FW

: Eau de mouillage

AIR

: Aspiration

LIGNE	DE	VERS	PRODUIT	TRANSPORT	SECTION	INSTRUMENTS
Gr-201	Élévateur M-201	S-203 Balance+Aimant	Grain brut	Élévateur à godets	Nettoyage	M-201, SC-201, FT-201
Gr-202	S-203 Balance+Aimant	Séparateur C-201	Grain	Gravité	Nettoyage	FIG-201
Gr-203	Séparateur C-201	Épierreur C-202	Grain	Gravité	Nettoyage	FIG-202, PDT-201
Gr-204	Épierreur C-202	Trieur C-203	Grain	Gravité	Nettoyage	FIG-203, P-201
Gr-205	Trieur C-203	Brosse C-204	Grain	Gravité	Nettoyage	FIG-204, P-202
Gr-206	Brosse C-204	Élévateur M-202	Grain conditionné	Gravité	Nettoyage	FT-204/205, FV-203/204/205
Gr-207	Élévateur M-202	Vis Mouilleur S-201	Grain	Élévateur à godets	Nettoyage	M-202, SC-202, FT-202, FC-201, FV-201
Gr-210	Élévateur M-203	Vis Mouilleur S-202	Grain	Élévateur à godets	Nettoyage	M-203, SC-203, FT-203, FC-202, FV-202
FW-201	Alimentation eau	S-201 / S-202	Eau de mouillage	Tuyauterie eau	Nettoyage	—
AIR-201	Réseau aspiration	C-201 / C-202	Aspiration	Conduite aspiration	Nettoyage	PDT-201

NOTES

- Repérage des instruments inspiré selon ISA-5.1.
- Liaisons de signal en pointillés verts.
- Tuyauteries procédé et eau : INOX ; aspiration : acier galvanisé.
- LT-202 pilote SC-202 / SC-203 (vitesse de M-202 / M-203) ;

- LSH-201 / LSH-202 : sécurité de niveau haut (arrêt remplissage).
5. Mouillage : boucles FT → FC → FV sur S-201 et S-202.
6. Extraction du silo régulée par FT → FC → FV sur chaque trémie.

PSEUDO-P&ID		
SCHÉMA LIGNE DE NETTOYAGE		
PROJET	N° DE PLAN	FORMAT
DESSINATEUR		DATE
VERSION	ÉCHELLE	FEUILLE 2 / 4